


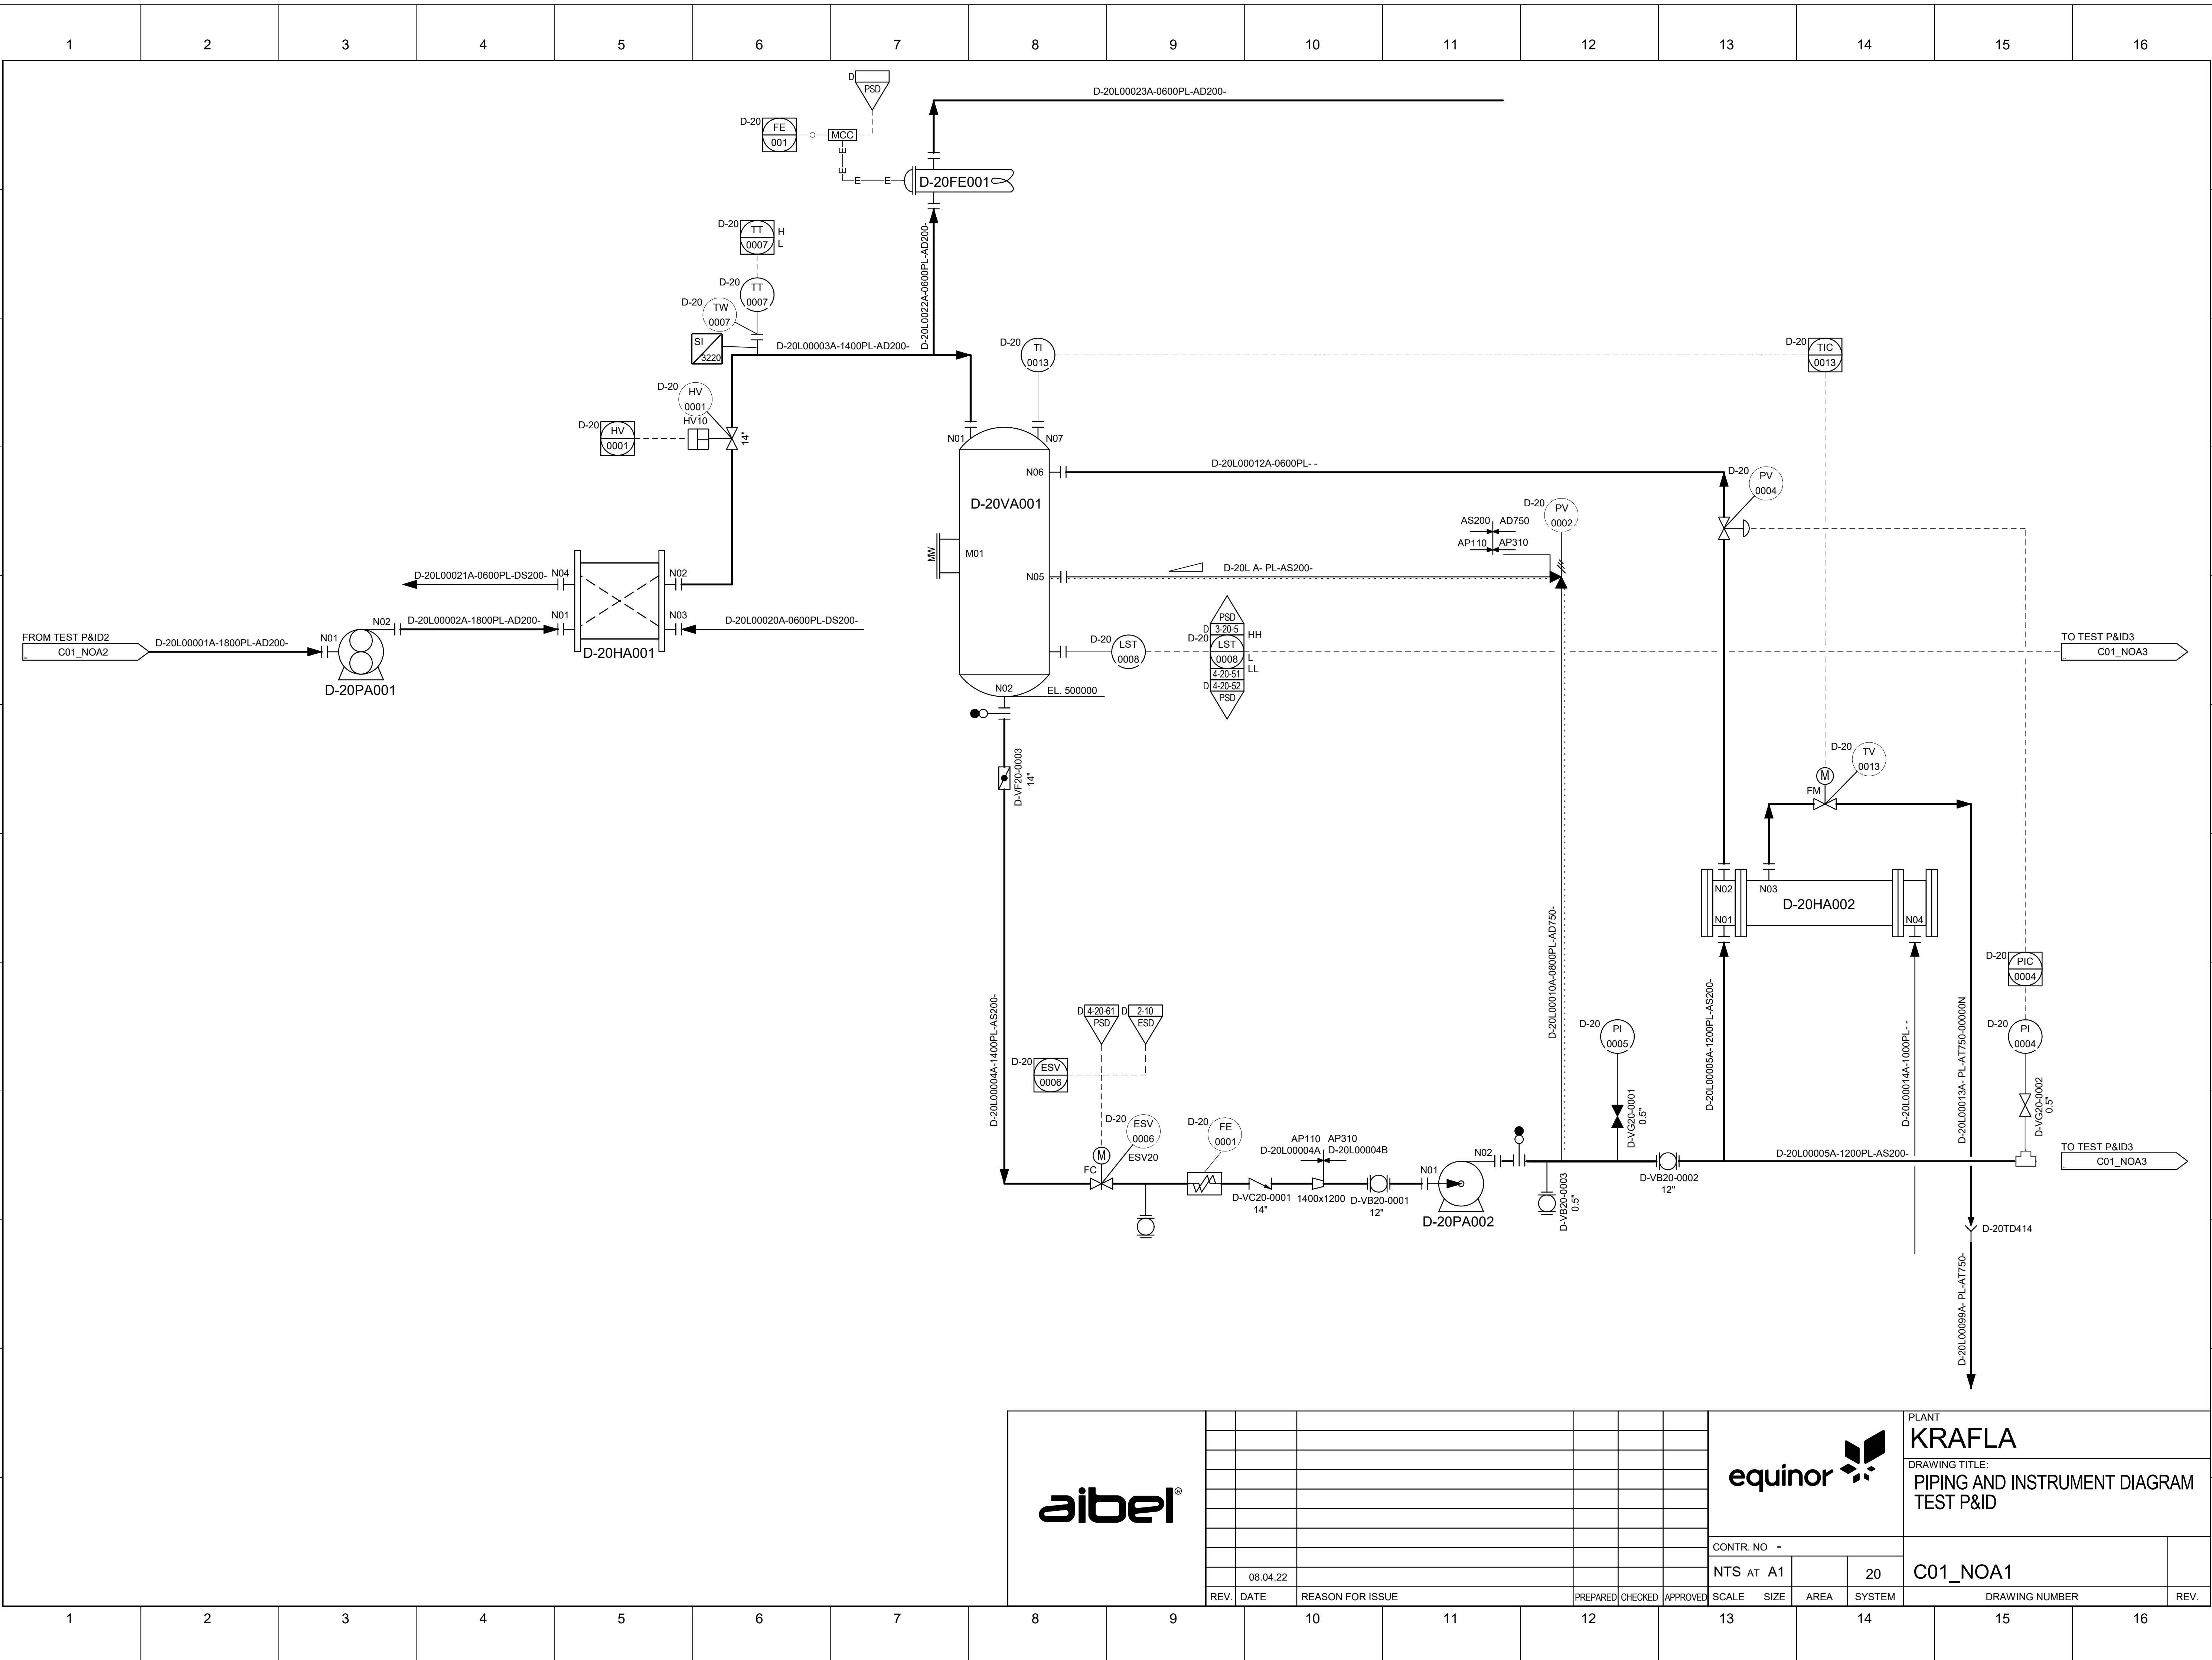

											PLANT KRAFLA				
											DRAWING TITLE: PIPING AND INSTRUMENT DIAGRAM TEST P&ID				
											CONTR. NO -				
	08.04.22									NTS AT A1		20	C01_NOA1		
REV.	DATE	REASON FOR ISSUE				PREPARED	CHECKED	APPROVED	SCALE	SIZE	AREA	SYSTEM	DRAWING NUMBER		REV.